




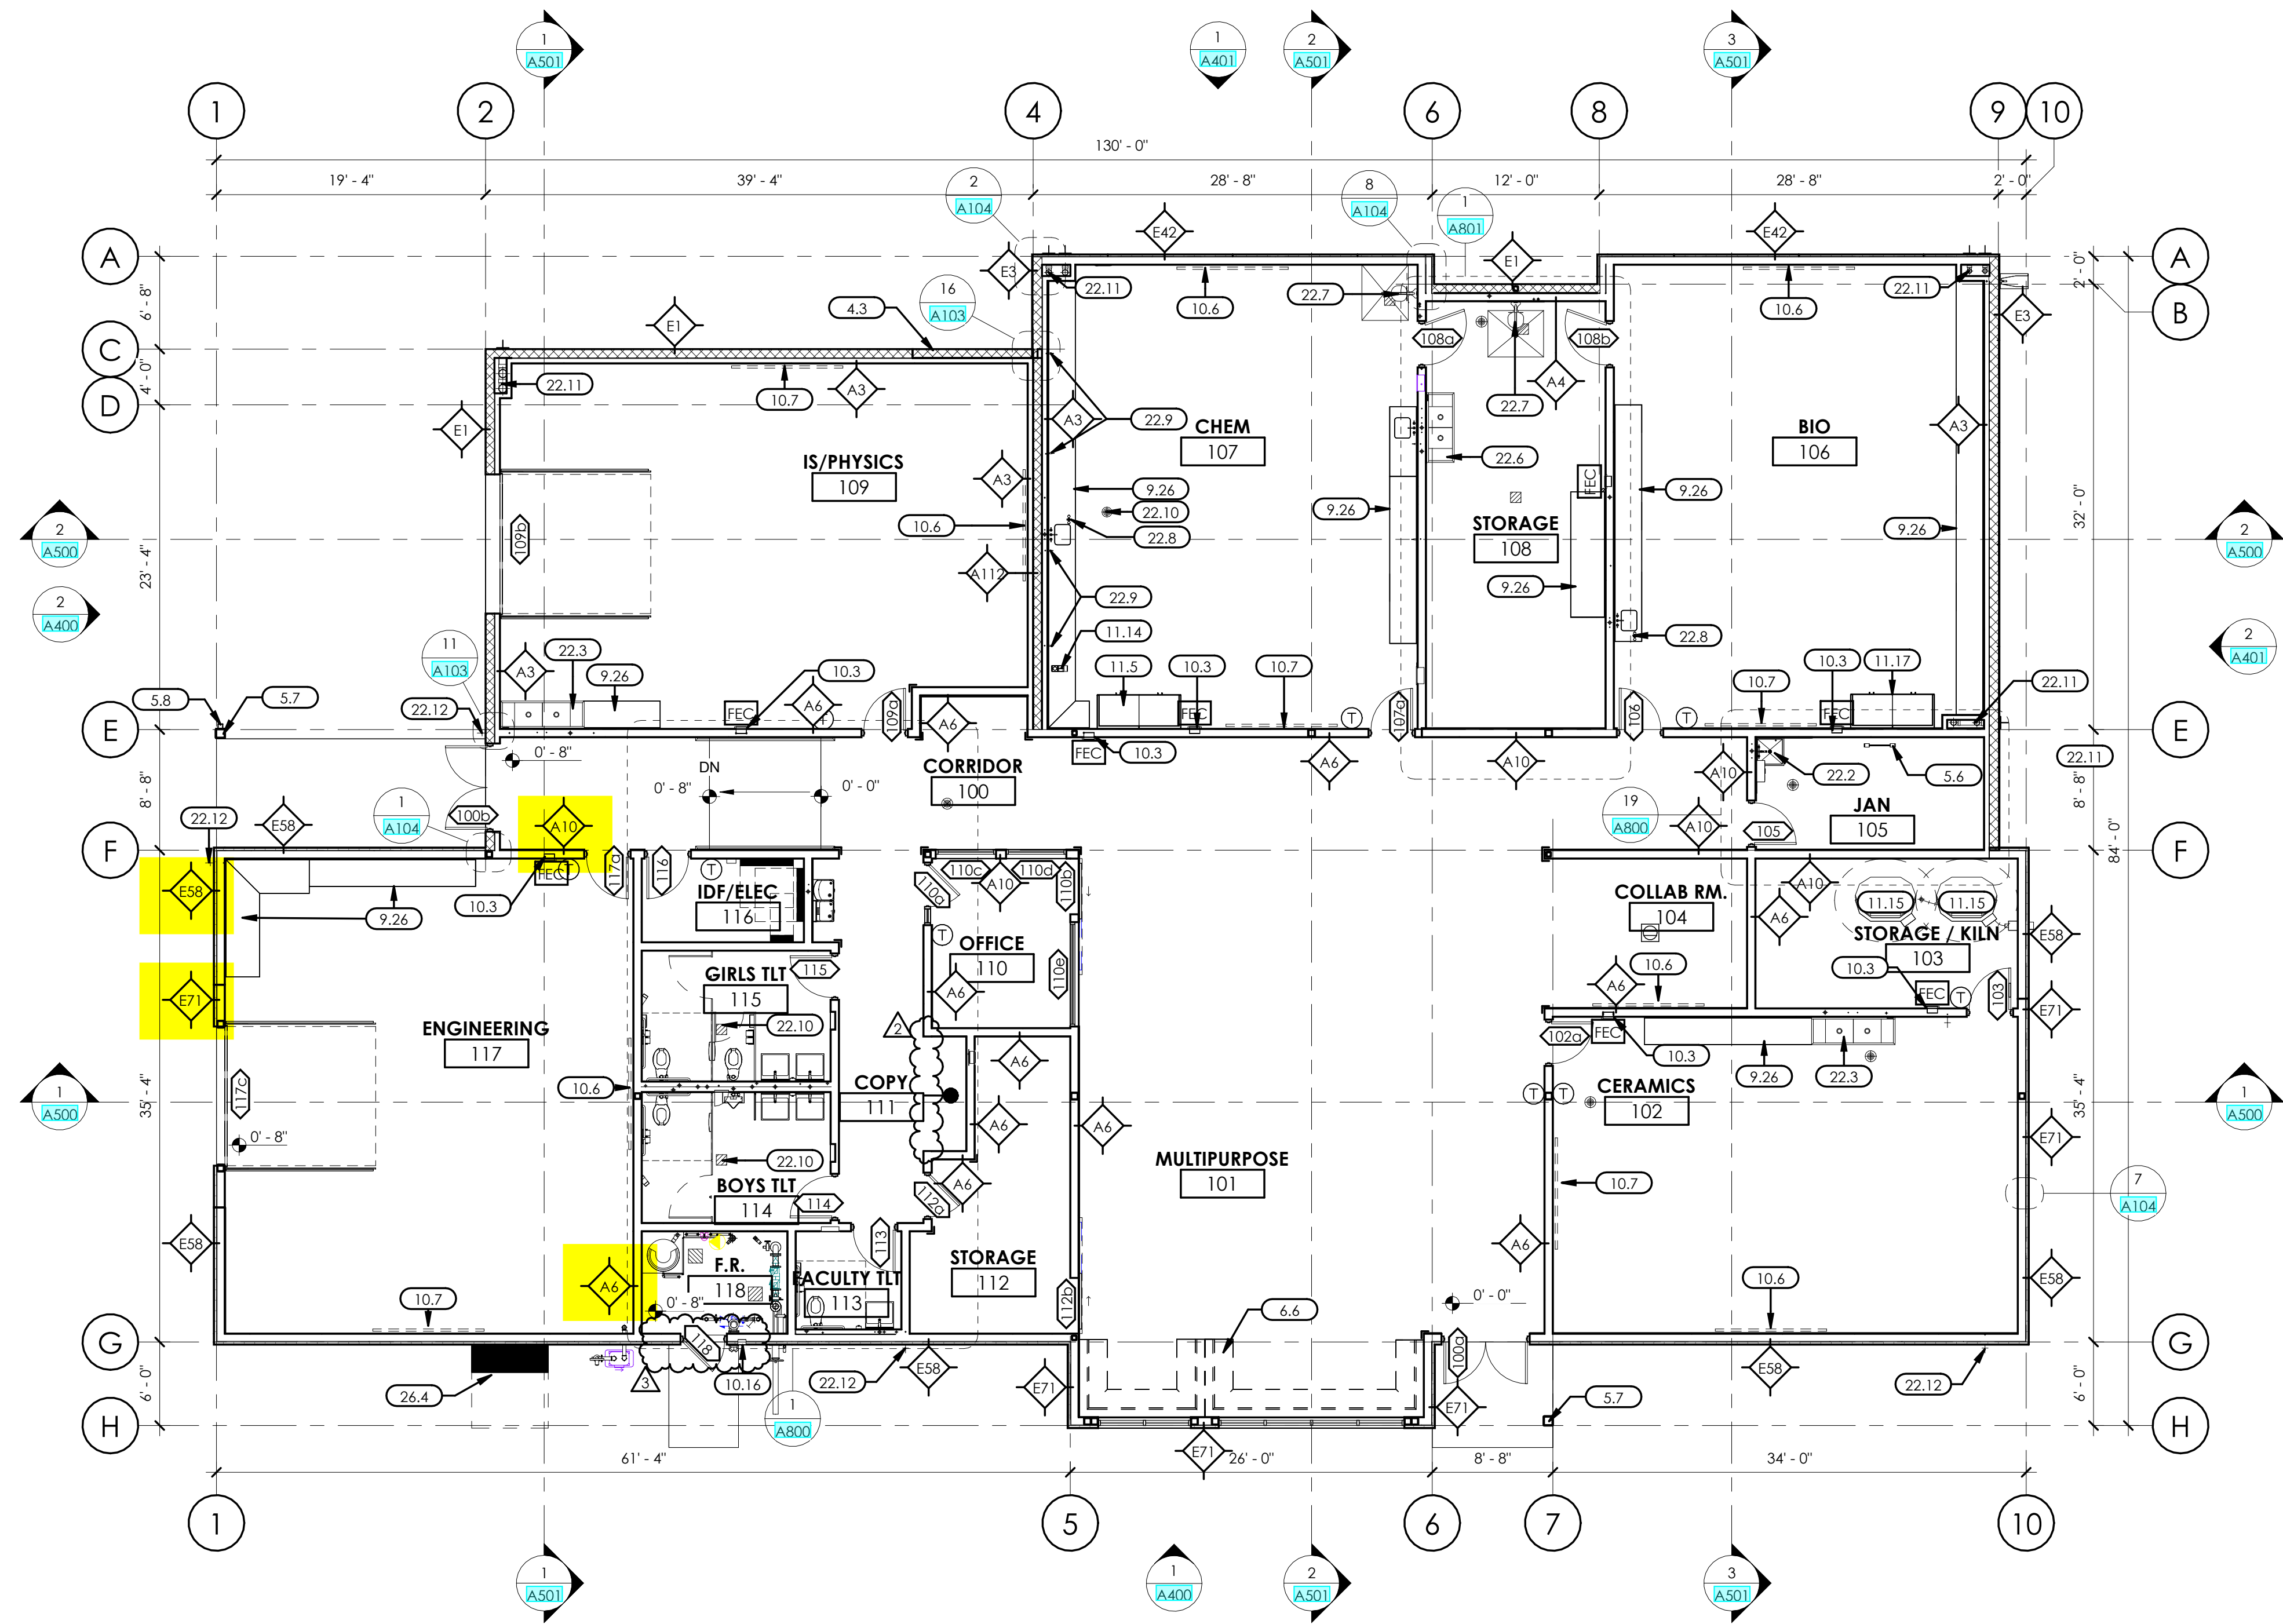

1 FLOOR PLAN - FIRST FLOOR
1/8" = 1'-0"

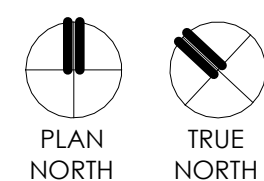

2 KEY PLAN - FIRST FLOOR
1/32" = 1'-0"

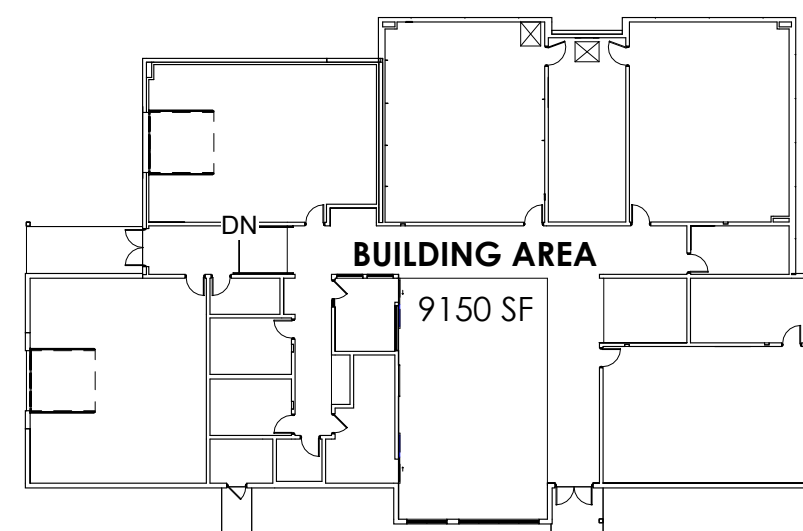


- KEY NOTES**
- 4.3 KNOCK-OUT PANEL, REFER TO STRUCTURAL
 - 5.6 ROOF ACCESS LADDER
 - 5.7 STEEL COLUMN, REFER TO STRUCTURAL
 - 5.8 DOWNSPOUT
 - 6.6 BUILT-IN BOOTH SEATING, SEE DETAIL 11/A906. REFER TO ELECTRICAL PLANS FOR POWER LOCATIONS - ADD ALTERNATE.
 - 9.26 MILLWORK WITH FINISH AS SPECIFIED. REFER TO ELEVATIONS FOR MORE INFORMATION.
 - 10.3 SEMI-RECESSED FIRE EXTINGUISHER CABINET
 - 10.6 WALL MOUNTED WHITE BOARD (96" X 48") MOUNT AT 3'-0" A.F.F. WP-1 REFER TO FINISH LEGEND
 - 10.7 ADD ALT. - WALL MOUNTED WHITE BOARD (96" X 48") MOUNT AT 3'-0" A.F.F. WP-1 REFER TO FINISH LEGEND
 - 10.16 FIRE DEPARTMENT KNOX BOX
 - 11.5 EXISTING FUME HOOD RELOCATED FROM EXISTING BUILDING. COORDINATE WITH MECHANICAL
 - 11.14 NEW VACUUM PUMP AS SPECIFIED TO BE COORDINATED WITH MPE OFCI.
 - 11.15 ELECTRIC KILN (1) EXISTING (1) NEW AS SPECIFIED OFCI.
 - 11.17 NEW FUME HOOD AS SPECIFIED. COORDINATE WITH MECHANICAL
 - 22.2 JANITOR SINK AND FAUCET. REFER TO PLUMBING DRAWINGS
 - 22.3 LARGE TROUGH SINK REFER TO PLUMBING DRAWINGS
 - 22.6 TROUGH SINK AS SPECIFIED REFER TO PLUMBING DRAWINGS
 - 22.7 COMBINATION EMERGENCY EYE-WASH AND DRENCH SHOWER REFER TO PLUMBING SCHEDULE
 - 22.8 DECK MOUNTED EYEWASH FIXTURE REFER TO PLUMBING DRAWINGS
 - 22.9 SINGLE VALVE LABORATORY TURRET AS SPECIFIED. REFER TO PLUMBING DRAWINGS
 - 22.10 FLOOR DRAIN - REFER TO PLUMBING DRAWINGS
 - 22.11 ROOF DRAIN LEADER. REFER TO PLUMBING DRAWINGS
 - 22.12 HOSE BIB. REFER TO PLUMBING DRAWINGS
 - 26.4 SES - REFER TO ELECTRICAL

- GENERAL NOTES**
1. DO NOT SCALE DRAWINGS. WRITTEN DIMENSIONS GOVERN. ALL PARTITION LOCATIONS SHALL BE AS SHOWN ON FLOOR PLAN. IN CASE OF CONFLICT, NOTIFY ARCHITECT.
 2. SEE SITE PLAN FOR WORK OUTSIDE OF THE BUILDING PERIMETER.
 3. IN-WALL INSULATION NOT SHOWN ON FLOOR PLANS FOR DRAWING CLARITY. REFER TO DETAILS AND WALL TYPES FOR ADDITIONAL INFORMATION.
 4. ALL DIMENSIONS ARE TO FACE OF MASONRY WALL, GRID, FACE OF SHEATHING, FACE OF STUD OR CENTER OF OPENING U.N.O.
 5. INTERIOR DOOR OPENINGS NOT LOCATED BY DIMENSIONS SHALL BE OFFSET 4" FROM FACE OF PERPENDICULAR WALL.
 6. FOR INTERIOR WALL HEIGHT INFORMATION SEE REFLECTED CEILING PLANS AND WALL TYPE DETAILS.
 7. WHERE PIPES, CONDUITS, AND OTHER PENETRATIONS ARE EXPOSED TO VIEW, PROVIDE ESCUTCHEONS, TYPICAL AT ALL WALLS, FLOORS, CEILINGS, ETC.
 8. CONTRACTOR SHALL PROTECT EXISTING CONSTRUCTION, FINISHES & EQUIPMENT TO REMAIN FROM DAMAGE DUE TO DEMOLITION AND CONSTRUCTION ACTIVITIES. ANY DAMAGE SUSTAINED DURING CONSTRUCTION ACTIVITY TO BE REPAIRED TO LIKE NEW CONDITIONS TO MATCH ADJACENT FINISHES & CONSTRUCTION.
 9. ALL UTILITIES, UNDERGROUND LINES AND PIPING TO BE ABANDONED SHALL BE PROPERLY DISCONNECTED, PLUGGED, CAPPED, AND TAGGED FOR EASY LOCATION AND IDENTIFICATIONS. COMPLY WITH CODE REQUIREMENTS AND SOUND CONSTRUCTION PRACTICE.
 10. PREVENT SPREAD OF DUST, FUMES AND SMOKE TO OTHER PARTS OF THE BUILDING AND NEIGHBORING PROPERTIES. CARRY OUT DEMOLITION WORK TO CAUSE AS LITTLE INCONVENIENCE TO ANY ADJACENT OCCUPIED BUILDINGS OR SITE AREAS AS POSSIBLE AND WITH MINIMUM INTERFERENCE TO PUBLIC OR PRIVATE ACCESSSES. MAINTAIN PROTECTED EGRESS AND ACCESS AT ALL TIMES. COORDINATE WITH OWNER AS NECESSARY.
 11. CONTRACTOR SHALL COORDINATE ANY REQUIRED UTILITY SHUTOFFS WITH THE OWNER.
 12. PROVIDE BLOCKING OR METAL STRAPPING AT ALL WALL-MOUNTED CABINETS, MARKER BOARDS, DISPLAY BOARDS, FIRE EXTINGUISHER CABINETS, WALL-BRACED EQUIPMENT, ETC.
 13. FOR FINISH MATERIALS AND LOCATIONS REFER TO FINISH PLANS, INTERIOR ELEVATIONS, AND FINISH DETAILS.
 14. SEE ENLARGED PLANS AND INTERIOR ELEVATIONS FOR MILLWORK INFORMATION.

THIS DRAWING IS AN INSTRUMENT OF SERVICE & IS THE PROPERTY OF SPS+ARCHITECTS LLP & MAY NOT BE REPRODUCED OR REPRODUCTIONS HEREOF USED WITHOUT WRITTEN PERMISSION.

REVISIONS		
MARK	DATE	DESCRIPTION
2	6/21/24	ASI-01
3	7/24/27	ASI-02

REVIEWED BY: AT
DRAWN BY: ALP

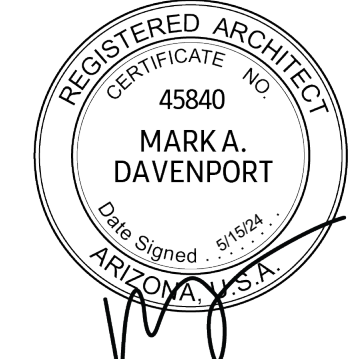

CONSTRUCTION SET
ASI 01 06-21-2024

JOB No: K2300049

SHEET:

A100

STEAM CLASSROOM BUILDING
NORTHLAND PREPARATORY ACADEMY
3300 SPARROW AVE
FLAGSTAFF, AZ 86004
OVERALL FLOOR PLAN - FIRST FLOOR

SPS+ ARCHITECTS
ARCHITECTS
219 N. 3RD AVENUE, SUITE 111
TUCSON, AZ 85705
P: 520.426.1180
F: 520.426.1180